



VÁŠ DOPIS ZN.:

SPISOVÁ ZNAČKA: SZ ÚMČ P15 00434/2021

ČJ.: 12428/2021/OD/MBu

VYŘIZUJE: Ing.Bureš

TEL.: 281 003 604

FAX: 281 003 611

E-MAIL: buresm@praha15.cz

DATUM: 23. 03. 2021

ÚŘAD MĚSTSKÉ ČÁSTI PRAHA 15

Vyvěšeno dne: Sejmuto dne:

24. 3. 2021

9. 4. 2021

Pořadové číslo: 1748

Počet listů: 10

VEŘEJNÁ VYHLÁŠKA

Oznámení o návrhu opatření obecné povahy pro stanovení místní úpravy provozu na pozemních komunikacích a výzva k uplatnění připomínek nebo námitek

Úřad městské části Praha 15, odbor dopravy příslušný podle § 124 odst. 6 zákona č. 361/2000 Sb., o provozu na pozemních komunikacích a o změnách některých zákonů (zákon o silničním provozu), ve znění pozdějších předpisů, a obecně závazné vyhlášky číslo 55/2000 Sb. hl. m. Prahy, kterou se vydává Statut hl. m. Prahy, ve znění pozdějších předpisů, v souladu s ust. § 171 a § 172 zákona č. 500/2004 Sb., správní řád, ve znění pozdějších předpisů, zahajuje dnešním dnem řízení o návrhu opatření obecné povahy, a předkládá

návrh opatření obecné povahy pro stanovení místní úpravy provozu na pozemních komunikacích

podle ust. § 77 odst. 1 písm. c) a odst. 5 zák. č. 361/2000 Sb., o provozu na pozemních komunikacích a o změnách některých zákonů (zákon o silničním provozu), ve znění pozdějších předpisů, a vyhlášky č. 294/2015 Sb., kterou se provádějí pravidla provozu na pozemních komunikacích, ve znění pozdějších předpisů, spočívající v úpravách a realizaci dopravního značení v oblasti ulic (MK III. třídy a účelových komunikací) **Na Košíku, Nad Košíkem a U Košíku MČ Praha 15, k.ú. Hostivař** (dle přiložených situací dopravního značení, které jsou nedílnou součástí tohoto návrhu opatření obecné povahy, z důvodu realizace obytné zóny a vyznačení parkovacích stání v předmětné oblasti za účelem umožnění parkování v souladu se zák. 361/2000 Sb., rezidentům předmětné oblasti, za níže uvedených podmínek pro jeho realizaci:

- Odbor dopravy ÚMČ Praha 15 si vyhrazuje právo případně vydané opatření obecné povahy pro stanovení místní úpravy provozu na pozemních komunikacích změnit, upravit, popřípadě zrušit, pokud si to vyžádá veřejný zájem nebo v případě, že dopravní značení bude umístěno v rozporu se stanovenými podmínkami.
- Odbor dopravy ÚMČ Praha 15 si vyhrazuje právo opatření obecné povahy nevydat a navrhovanou místní úpravu provozu na pozemních komunikacích nerealizovat.
- Realizace místní úpravy provozu bude v případě vydání opatření obecné povahy předpokládaná přibližně do 31. 05. 2021.

V souladu s ust. § 172 odst. 4 zákona č. 500/2004 Sb., správní řád, ve znění pozdějších předpisů, může kdokoli k návrhu uplatnit písemné připomínky, jestliže se domnívá, že jeho práva a povinnosti mohou být tímto opatřením přímo dotčeny (dále jen „dotčené osoby“). V souladu s dílcí ust. § 172 odst. 5 zákona č. 500/2004 Sb., správní řád, ve znění pozdějších předpisů, mohou k tomuto návrhu podat písemné odůvodněné námítky vlastníci nemovitostí, jejichž práva, povinnosti nebo zájmy mohou být tímto návrhem přímo dotčeny (dále jen „dotčené osoby“). Připomínky a námítky proti návrhu lze podat u Úřadu městské části Praha 15, odboru dopravy, Boloňská 478/1, 109 00 Praha 10.

Úřad městské části Praha 15, odbor dopravy, ve smyslu ust. § 172 odst. 1 zákona č. 500/2004 Sb.,

sídlo: Boloňská 478/1, 109 00 Praha 10

pracoviště: Boloňská 478/1, 109 00 Praha 10

bankovní spojení: ČS a.s., č.ú. 19-2000719399/0800

e-mail: podatelna@p15.mepnet.cz

http://www.praha15.cz

tel.: +420-281 003 111

fax: +420-274 864 756

IČ: 00231355

DIČ: CZ00231355

správní řád, ve znění pozdějších předpisů,

v y z ý v á

dotčené osoby, aby k návrhu opatření podávaly připomínky nebo námítky, a to ve lhůtě do 30 dnů ode dne zveřejnění tohoto návrhu.

Odůvodnění

ÚMČ Praha 15, odbor dopravy zahájil dnešním dnem řízení o návrhu opatření obecné povahy pro stanovení místní úpravy provozu, spočívající v úpravách a realizaci dopravního značení v oblasti ulic (MK III. třídy a účelových komunikací) **Na Košíku, Nad Košíkem a U Košíku MČ Praha 15, k.ú. Hostivař**, dle přiložené situace dopravního značení, jedná se o realizaci obytné zóny a vyznačení parkovacích stání v předmětné oblasti za účelem umožnění parkování v souladu se zák. 361/2000 Sb., rezidentům předmětné oblasti, za níže uvedených podmínek pro jeho realizaci.

Tento návrh opatření obecné povahy ke stanovení místní úpravy provozu bude vyvěšen na úřední desce Úřadu městské části Praha 15 po dobu 15 dnů.

OTISK RAZÍTKA

Zdeněk Havel v.r.
vedoucí odboru dopravy
ÚMČ Praha 15

Přílohy
Situace dopravního značení - 7 Listů

Obdrží

ÚMČ Praha 15- KÚT, zde (k vyvěšení na úřední desku – 15 dnů)

MČ Praha 15 - MO, zde

TSK hl. m. Prahy, a.s., Řásnovka 770/8, 110 15 Praha 1, IDS: mivq4t3

Policie ČR, KŘP hl. m. Prahy, OSDP, Kongresová 1666/2, 140 21 Praha 4

sídlo: Boloňská 478/1, 109 00 Praha 10

tel.: +420-281 003 111

fax: +420-274 864 756

pracoviště: Boloňská 478/1, 109 00 Praha 10


IČ: 00231355

DIČ: CZ00231355

bankovní spojení: ČS a.s., č.ú. 19-2000719399/0800

e-mail: podatelna@p15.mepnet.cz

http://www.praha15.cz

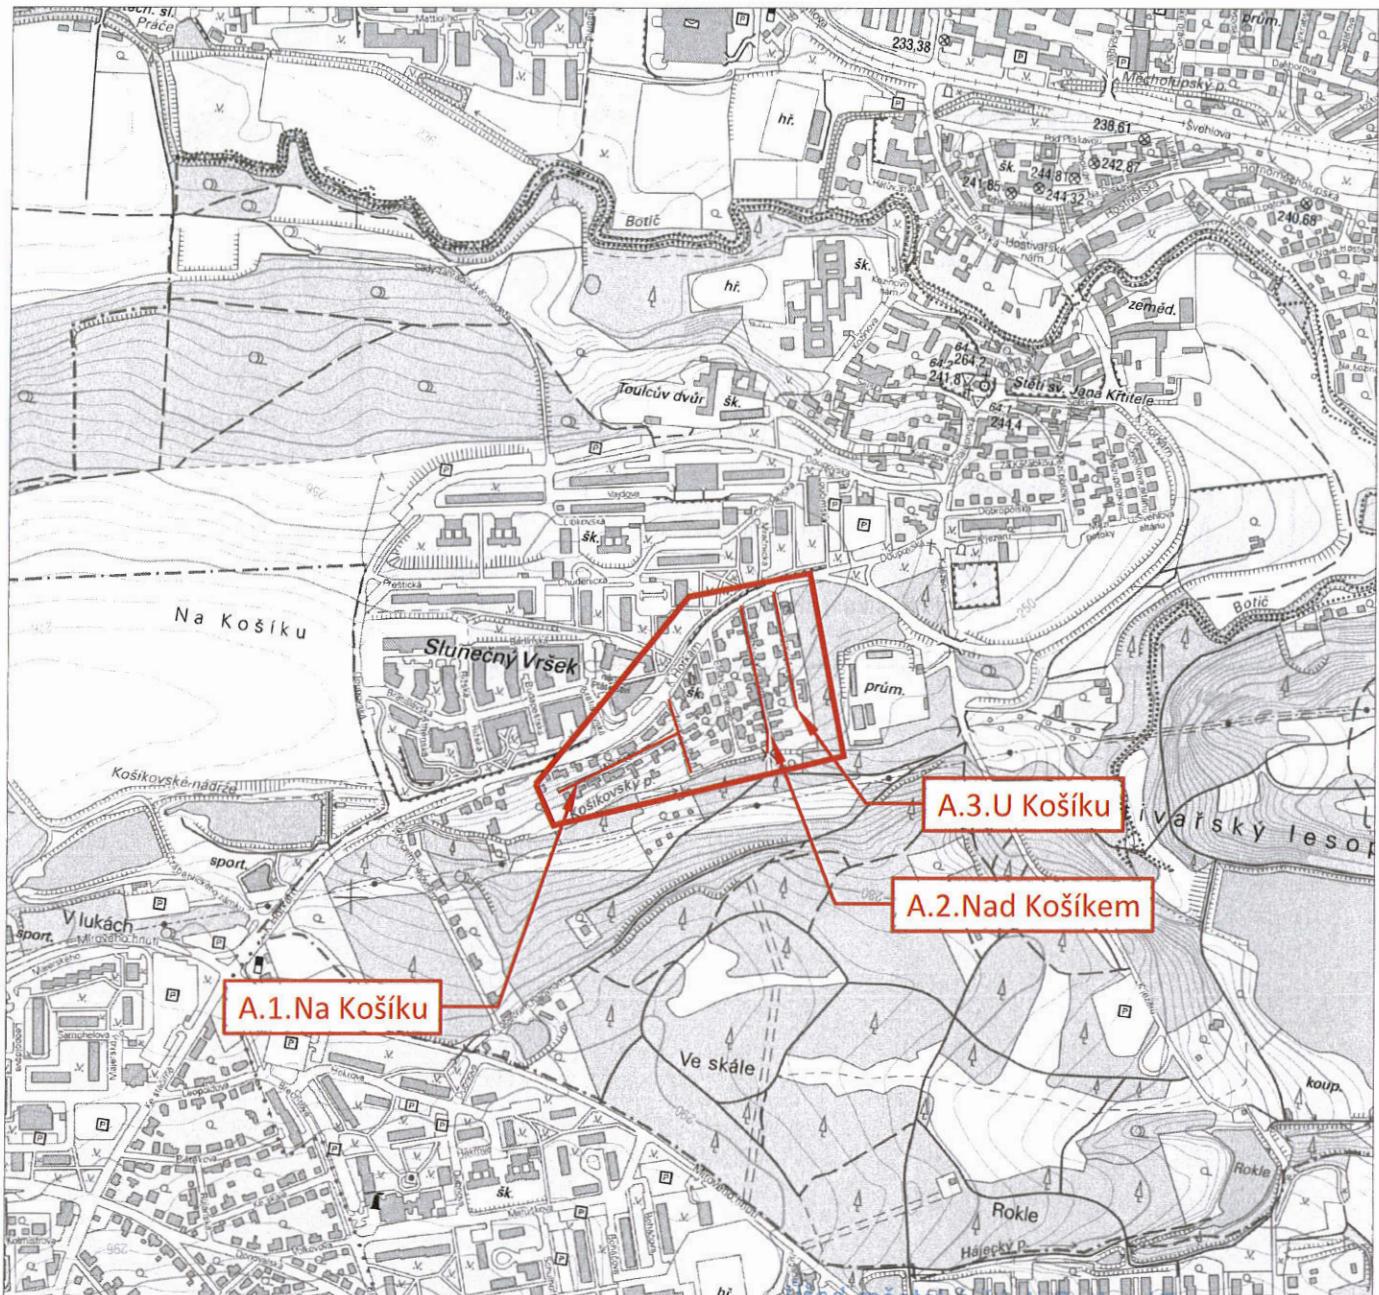

Úřad městské části Praha 15
odber dopravy 11
100 00 Praha 10, Boleňská 478
23.3.2021

Objednatel:

Jana Bažantová, Nad Košíkem 410/11, 102 00, Praha 10 - Hostivař

Hlavní projektant:

Sinpps s.r.o.



Stavebně inženýrské, projektové a poradenské služby
Dobrušská 1805/5, 147 00 Praha 4 • www.sinpps.cz
IČO: 62584332 DIČ: CZ62584332
zapsána v OR Praha oddíl C, vložka 33665

Hlavní inženýr projektu:

Ing. Pavel Jeřábek

Zodpovědný projektant:

Ing. Pavel Jeřábek

Kontroloval:

Ing. Jan Božovský

Vypracoval:

Ing. Tomáš Fial

Akce:

**Úprava dopravního režimu na
obytnou zónu v ulicích Na Košíku,
Nad Košíkem, U Košíku - Praha 15**

Číslo zakázky:
75-2020

Číslo kopie:

Datum:
11/2020

Stupeň:
ZPD

TENTO NÁVRH JE DUŠEVNÍM VLASTNICTVÍM AUTORA A JE CHRÁNĚN VE SMYSLU "AUTORSKÉHO ZÁKONA" (č.121/2000 Sb.)

Název akce:

Úprava dopravního režimu na obytnou zónu v ulicích Na Košíku, Nad Košíkem, U Košíku - Praha 15


Stupeň dokumentace:

ZPD (zjednodušená projektová dokumentace)

Seznam příloh

A Výkresová část

- A.1.a Situace stavby - Na Košíku
- A.1.b Situace stavby - Na Košíku - obalové křivky
- A.2.a Situace stavby - Nad Košíkem
- A.2.b Situace stavby - Nad Košíkem - obalové křivky
- A.3.a Situace stavby - U Košíku
- A.3.b Situace stavby - U Košíku - obalové křivky

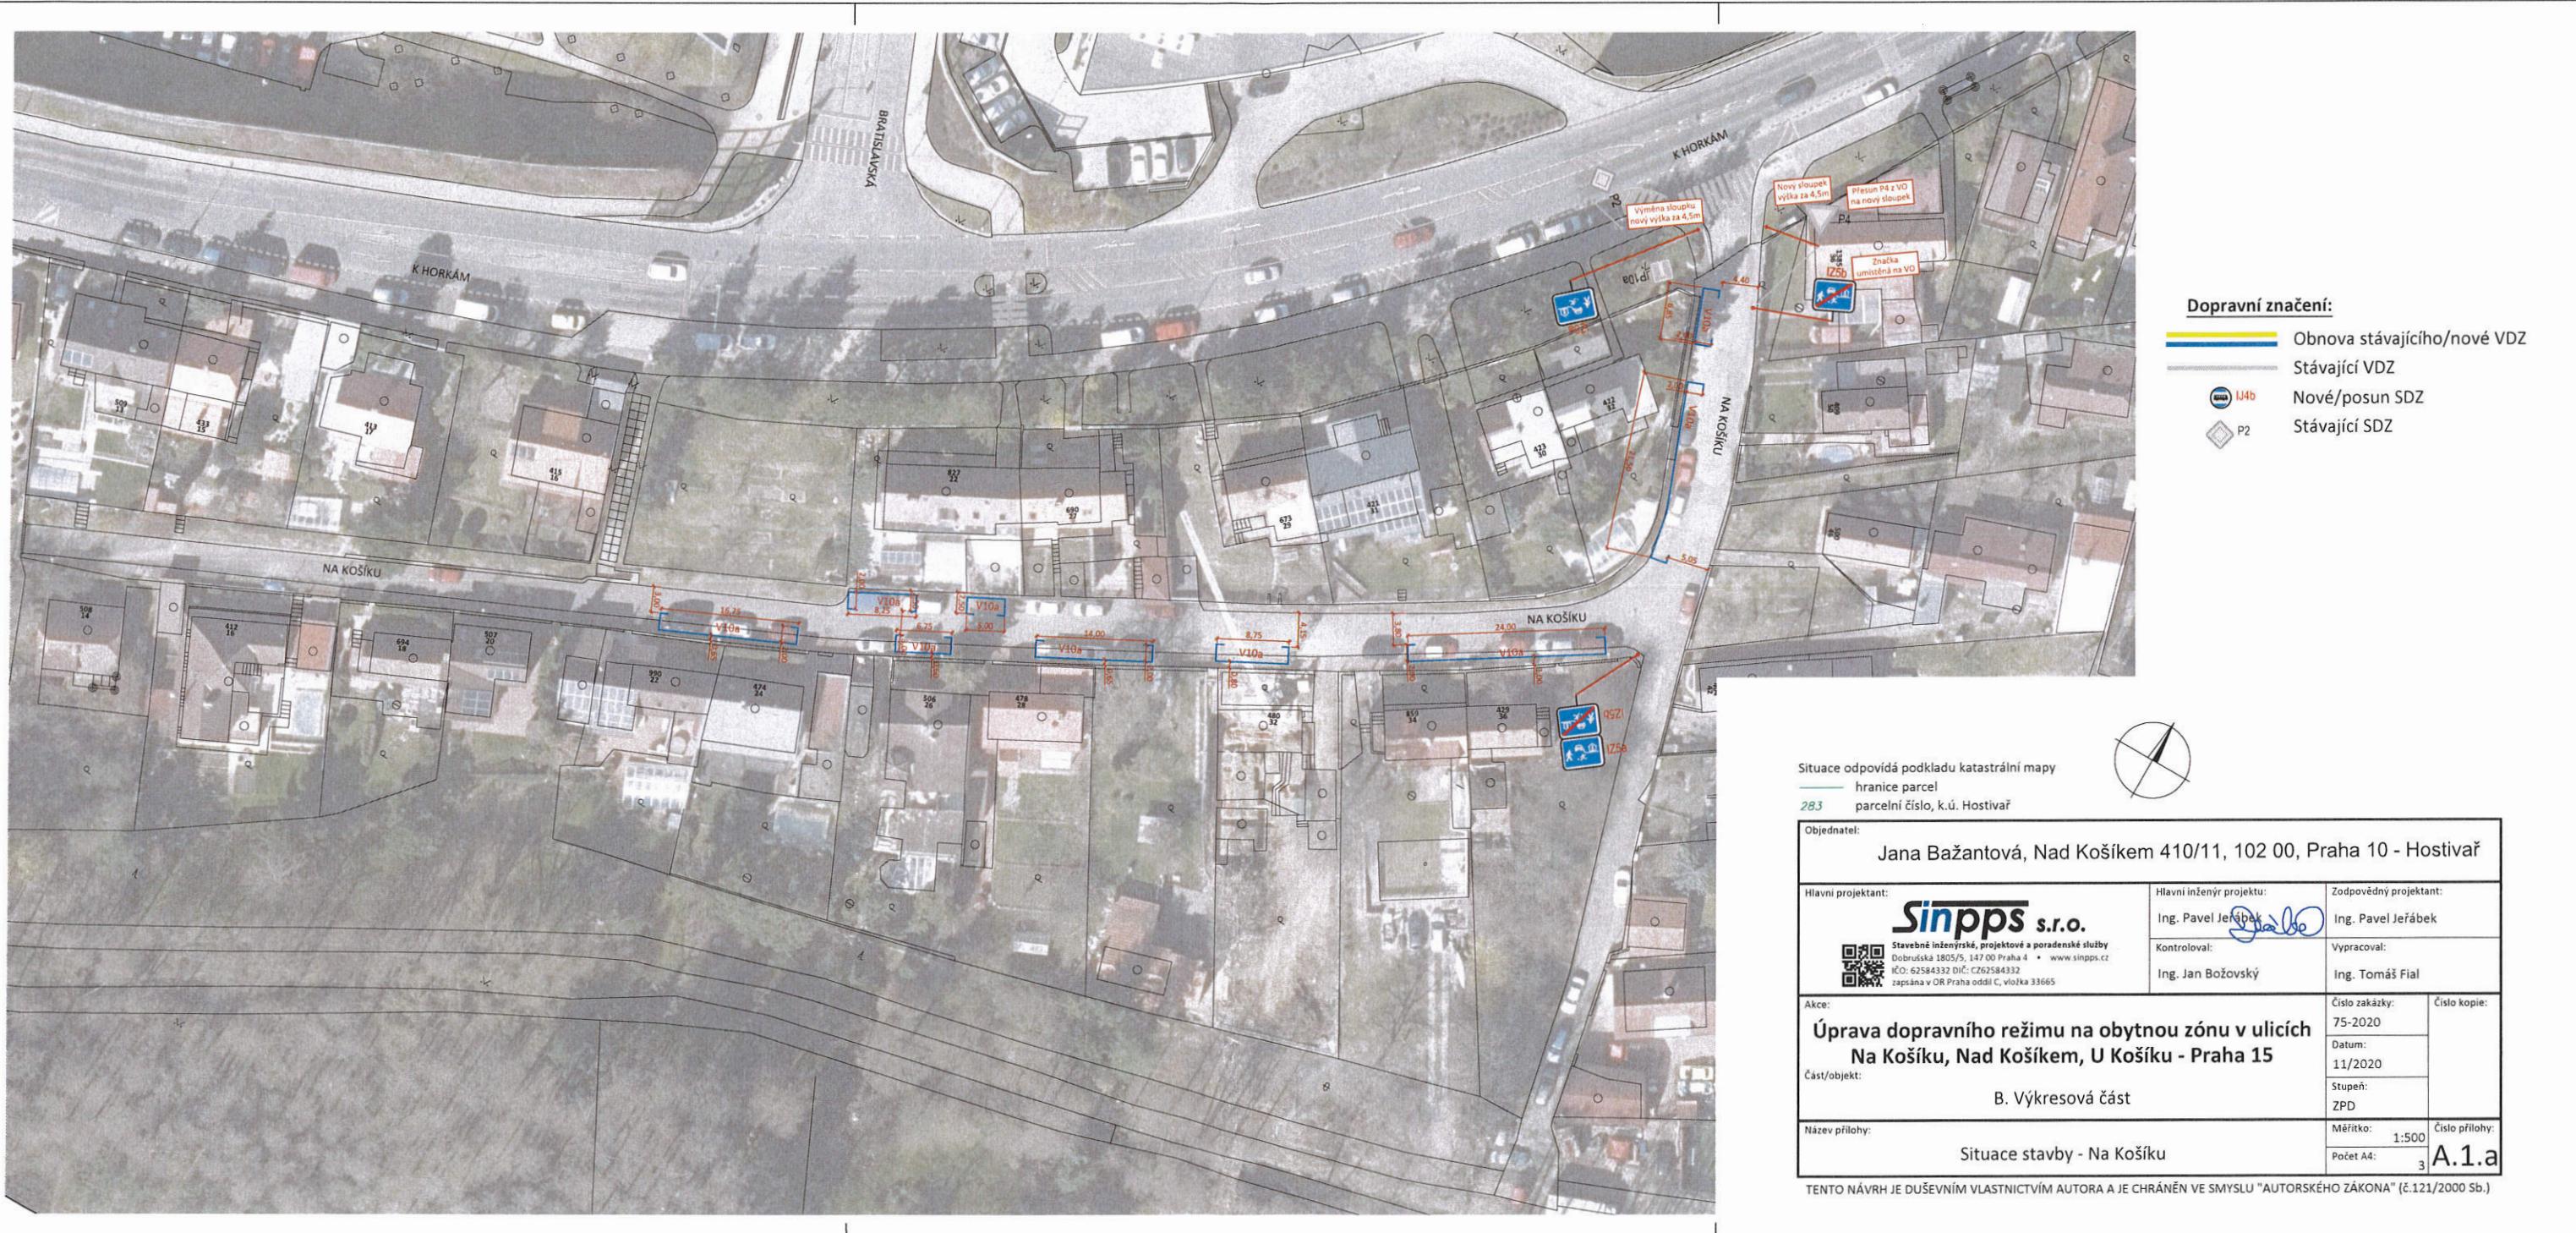

88434/2021
 úřad městské části Praha 15
 odbor dopravy
 109 00 Praha 10, Balabenkova 478

23.3.2021

D



Situace odpovídá podkladu katastrální mapy

hranice parcel

283 parcelní číslo, k.ú. Hostivař

Objednatel:

Jana Bažantová, Nad Košíkem 410/11, 102 00, Praha 10 - Hostivař

Hlavní projektant:

sinpps s.r.o.

Stavebně inženýrské, projektové a poradenské služby
Dobrušská 1805/5, 147 00 Praha 4 • www.sinpps.cz
IČO: 62584332 DIČ: CZ62584332
zapsána v OR Praha oddíl C, vložka 33665

Hlavní inženýr projektu:

Ing. Pavel Jeřábek

Zodpovědný projektant:

Ing. Pavel Jeřábek

Kontroloval:

Výpracoval:

Ing. Jan Božovský

Ing. Tomáš Fial

Číslo zakázky:

75-2020

Číslo kopie:

Datum:

11/2020

Stupeň:

ZPD

Měřítka:

1:500

Číslo přílohy:

Počet A4:

3 A.1.b

Akce:

Úprava dopravního režimu na obytnou zónu v ulicích
Na Košíku, Nad Košíkem, U Košíku - Praha 15

Část/objekt:

B. Výkresová část

Název přílohy:

Situace stavby - Na Košíku - obalové křivky

TENTO NÁVRH JE DUŠEVNÍM VLASTNICTVÍM AUTORA A JE CHRÁNĚN VE SMYSLU "AUTORSKÉHO ZÁKONA" (č.121/2000 Sb.)

Úřad městské části Praha 15
odbor dopravy
109 00 Praha 10, Bolonická 478


23.3.2021




00834/2021
Úřad městské části Praha 13
odbor dopravy

109 00 Praha 10, Bořislíkova 473

23.3.2021

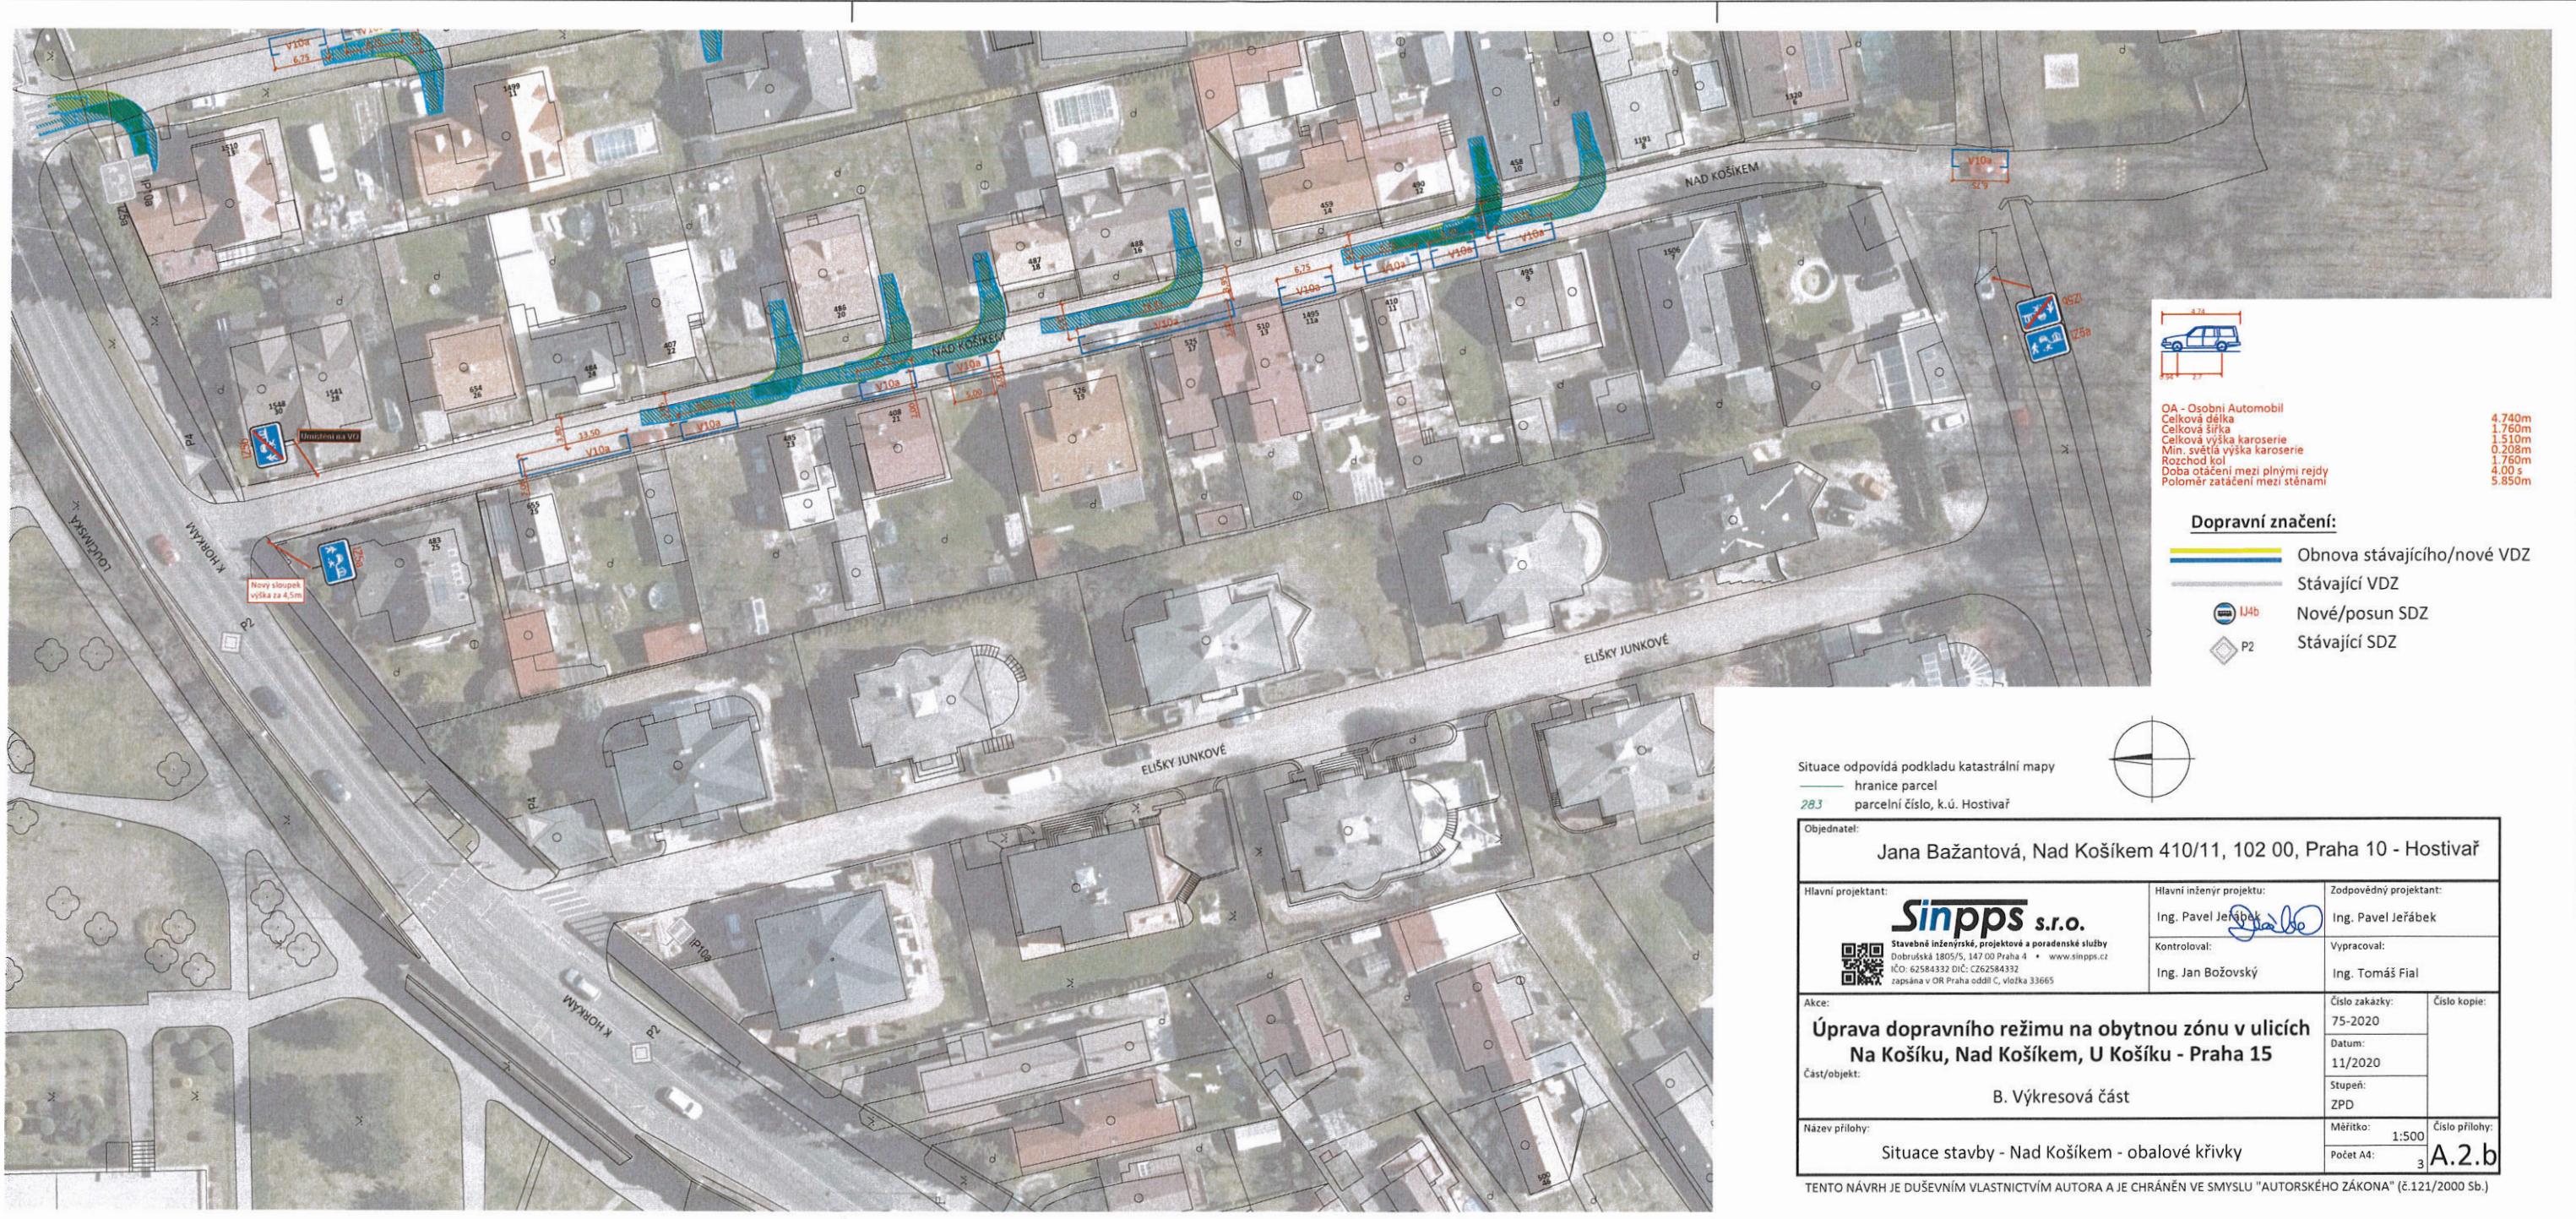

00434/2021
 Úřad městské části Praha 10
 odbor dopravy 11
 109 00 Praha 10, Boloňská 478
 28.3.2021 *[Signature]*

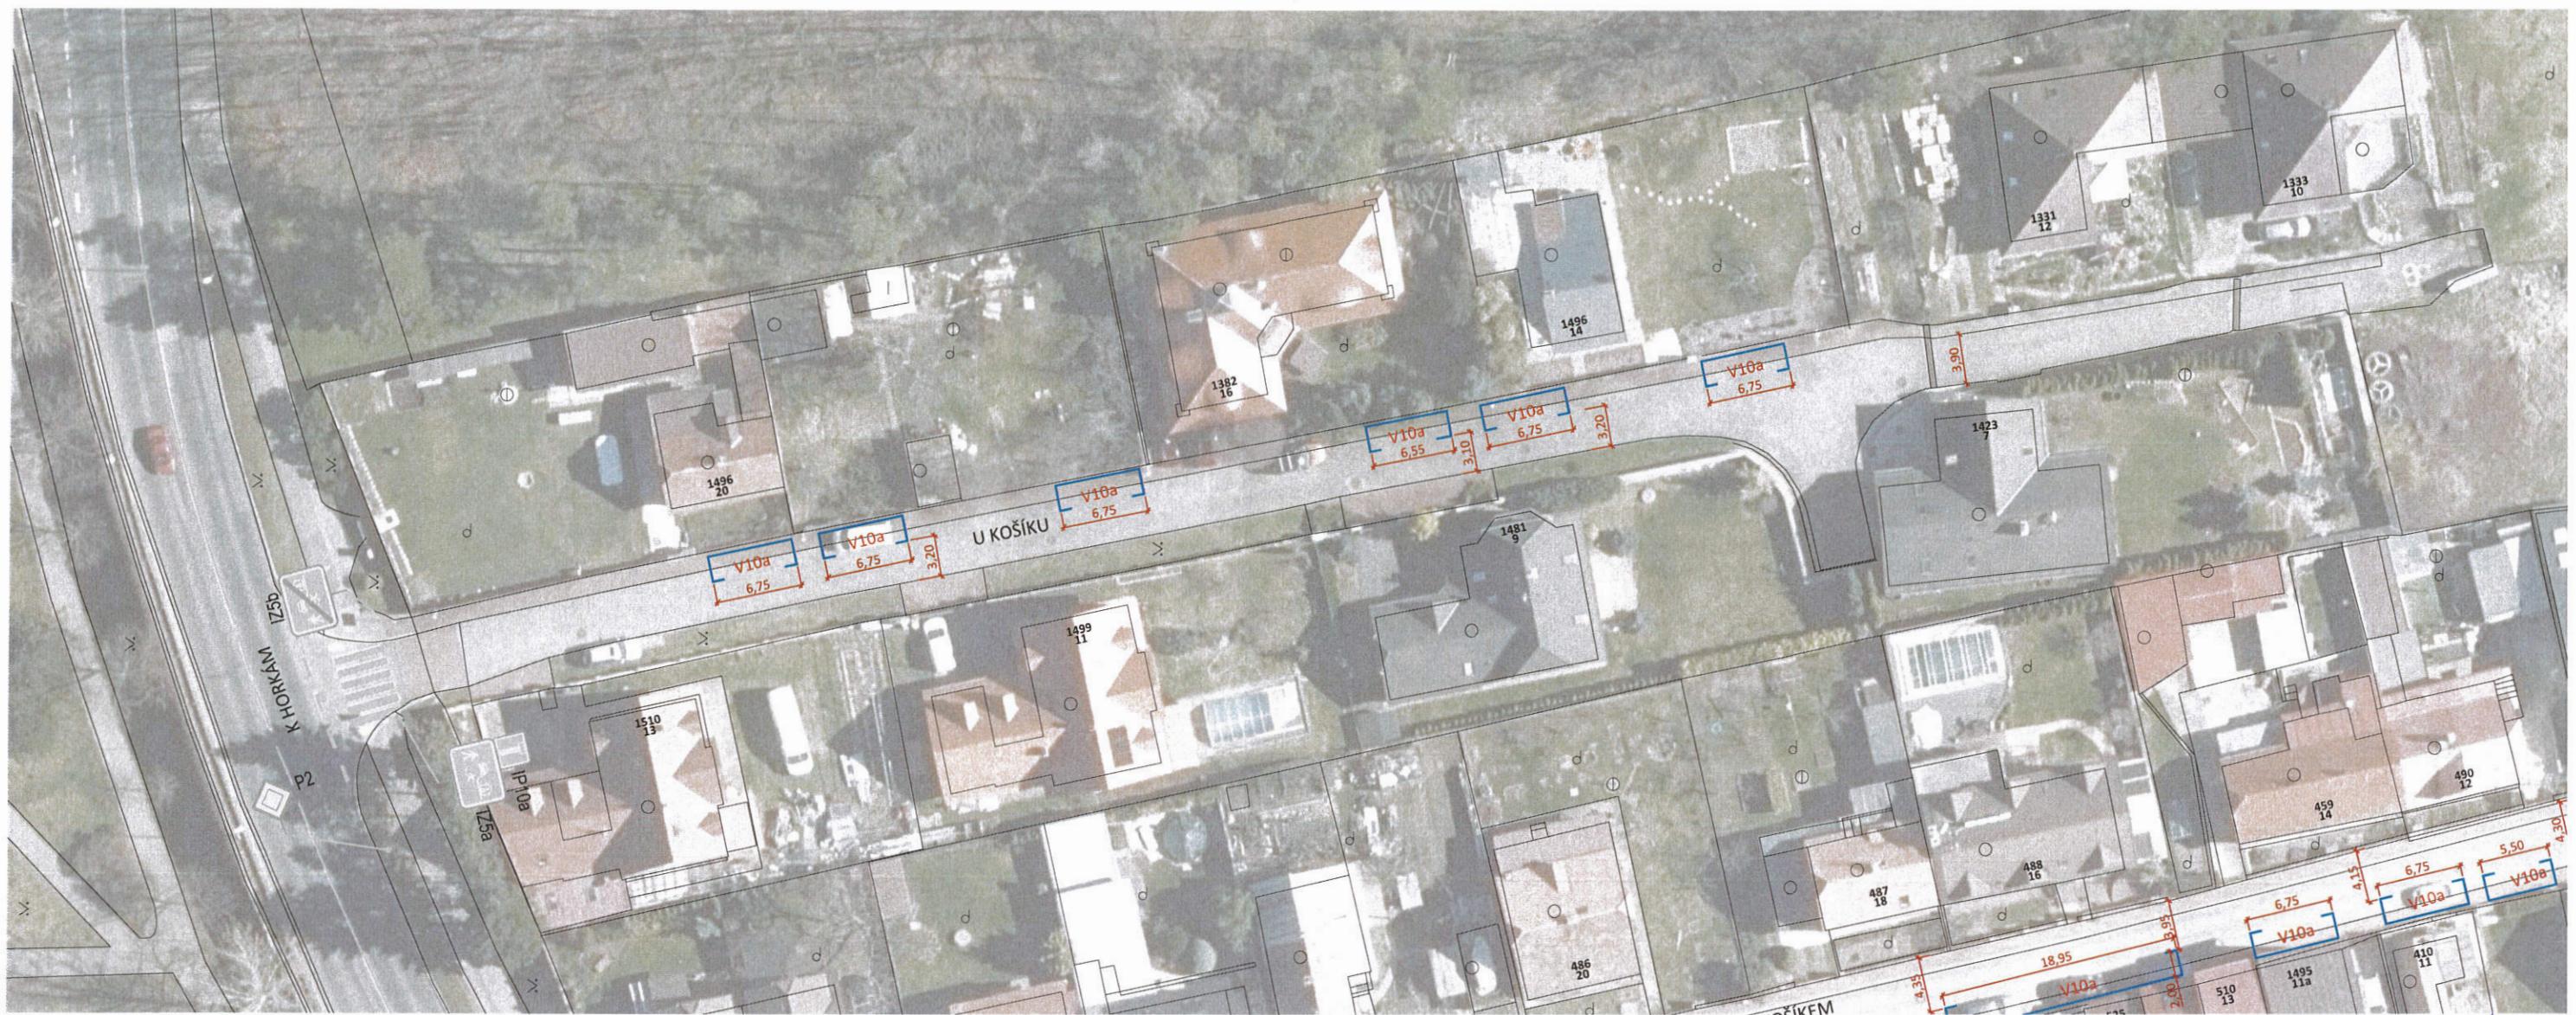

Dopravní značení:

- Obnova stávajícího/nové VDZ
- Stávající VDZ
- Nové/posun SDZ
- Stávající SDZ



IJ4b




P2

Situace odpovídá podkladu katastrální mapy

— hranice parcel

283 parcelní číslo, k.ú. Hostivař

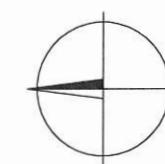

Úřad městské části Praha 15
odbor dopravy
109 00 Praha 10, Dobrušká 478

28.3.2021

J

Objednatel:

Jana Bažantová, Nad Košíkem 410/11, 102 00, Praha 10 - Hostivař

Hlavní projektant:

Sinpps s.r.o.

Stavebně inženýrské, projektové a poradenské služby
Dobrušká 1805/5, 147 00 Praha 4 • www.sinpps.cz
IČO: 62584332 DiČ: CZ62584332
zapsána v OR Praha oddíl C, vložka 33665

Hlavní inženýr projektu:

Ing. Pavel Jeřábek

Zodpovědný projektant:

Ing. Pavel Jeřábek

Kontroloval:

Ing. Jan Božovský

Vypracoval:

Ing. Tomáš Fial

Akce:

**Úprava dopravního režimu na obytnou zónu v ulicích
Na Košíku, Nad Košíkem, U Košíku - Praha 15**

Část/objekt:

B. Výkresová část

Název přílohy:

Situace stavby - U Košíku

Číslo zakázky:

75-2020

Datum:

11/2020

Stupeň:

ZPD


Měřítko:

1:500

Číslo přílohy:


A.3.a

2

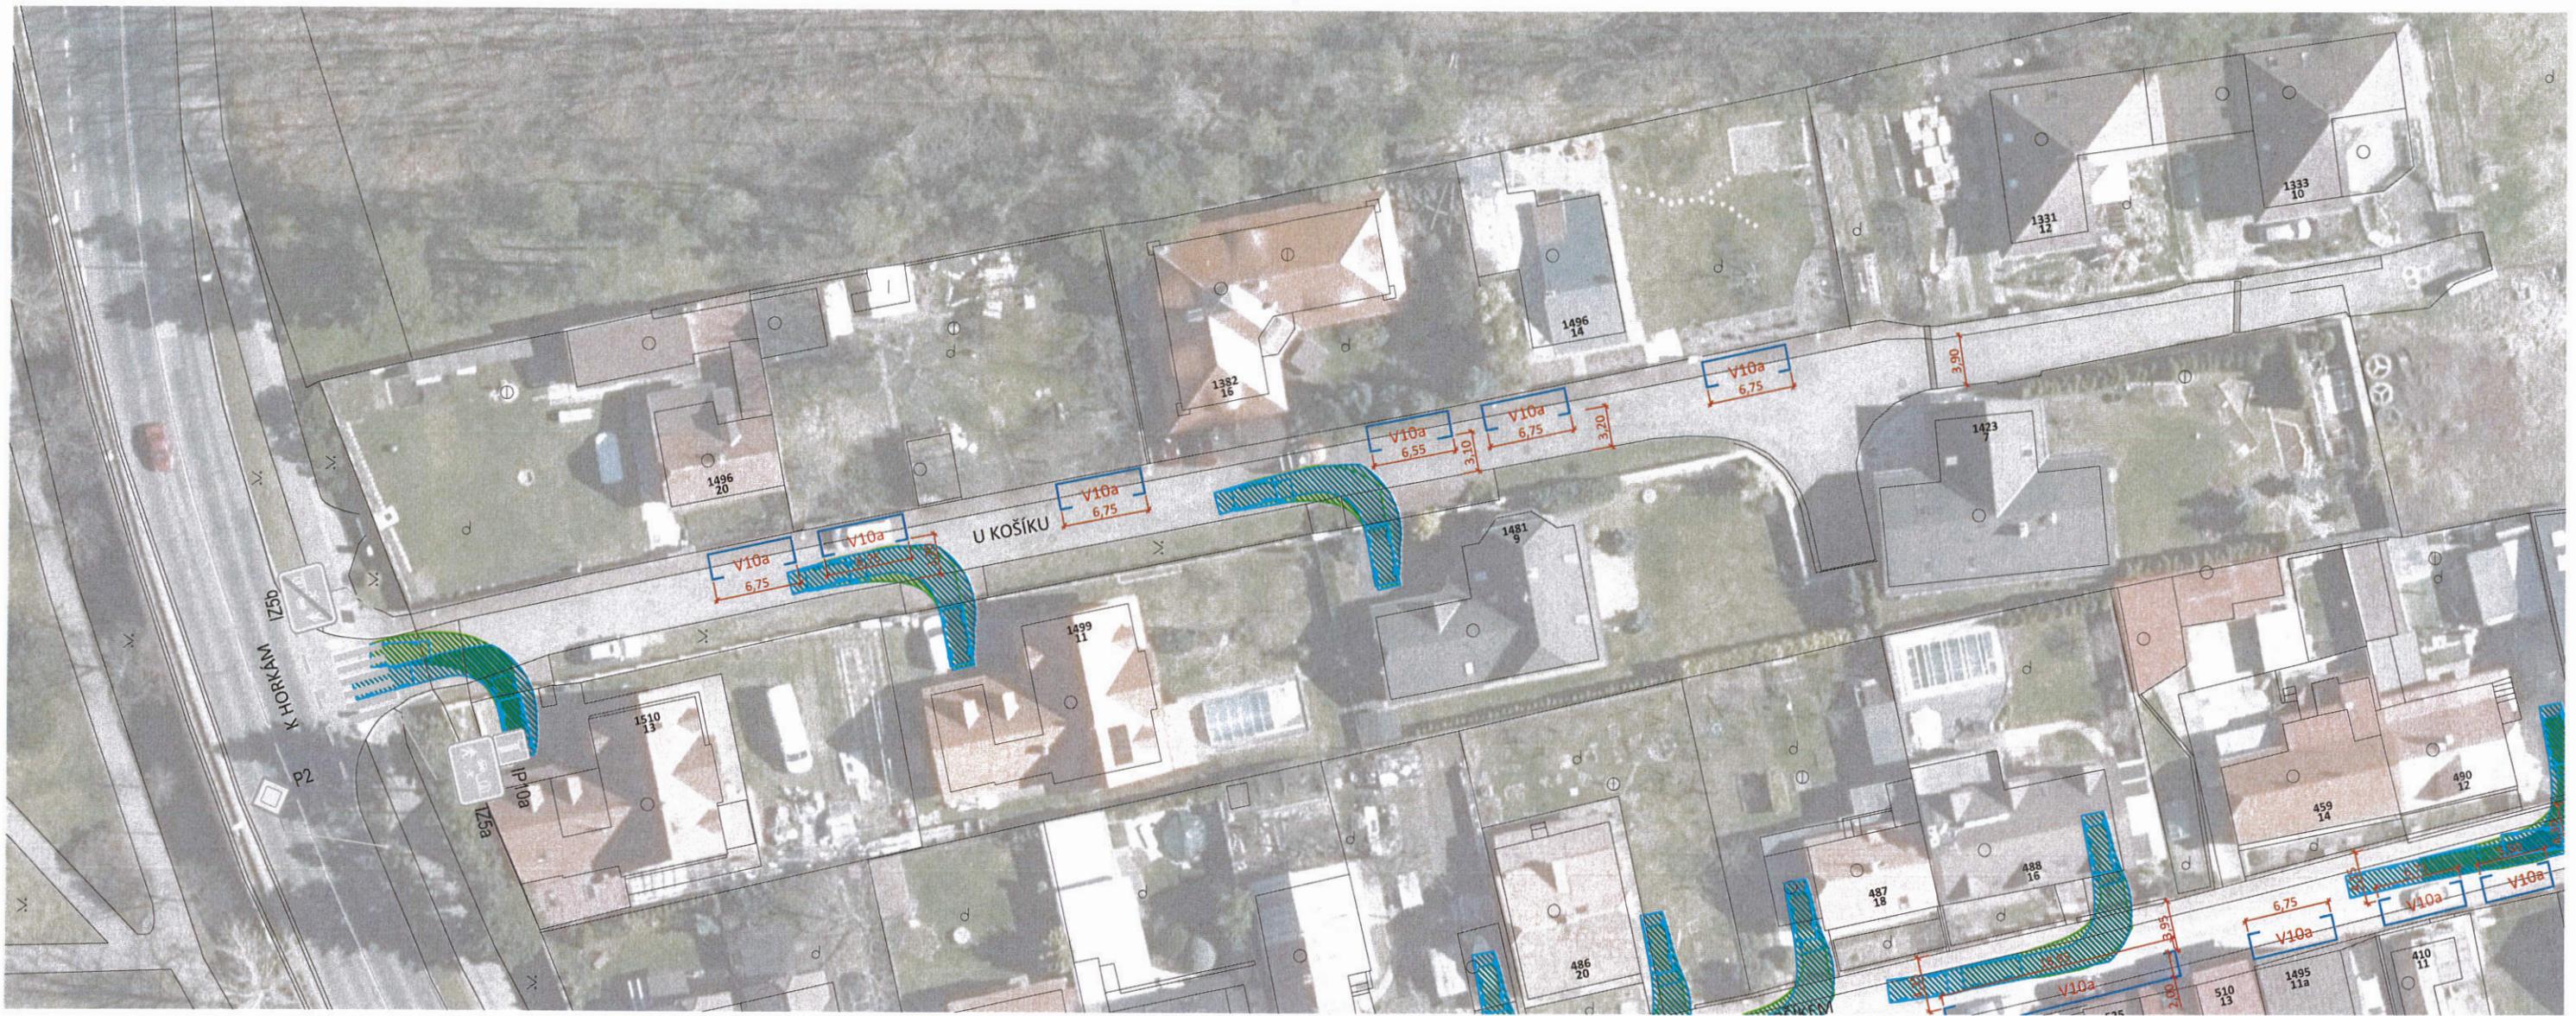

Dopravní značení:

- Obnova stávajícího/nové VDZ
- Stávající VDZ
- IJ4b
- P2
- Nové/posun SDZ
- Stávající SDZ

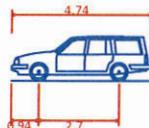

OA - Osobní Automobil
Celková délka
Celková šířka
Celková výška karoserie
Min. světlá výška karoserie
Rozchod kol
Doba otáčení mezi plnými rejdy
Poloměr zatáčení mezi stěnami

4.740m
1.760m
1.510m
0.208m
1.760m
4.00 s
5.850m

Situace odpovídá podkladu katastrální mapy

hranice parcel

283 parcelní číslo, k.ú. Hostivař



00434/2021

Úprava dopravního režimu na obytnou zónu v ulicích

Nad Košíkem, U Košíku - Praha 15

23.2.2021 (f)

Objednatel:

Jana Bažantová, Nad Košíkem 410/11, 102 00, Praha 10 - Hostivař

Hlavní projektant:	Hlavní inženýr projektu:	Zodpovědný projektant:
--------------------	--------------------------	------------------------

Sinpps s.r.o.

Stavebně inženýrské, projektové a poradenské služby
Dobrušská 1805/5, 147 00 Praha 4 • www.sinpps.cz
IČO: 62584332 DIČ: CZ62584332
zapsána v OR Praha oddíl C, vložka 33665

Kontroloval:	Vypracoval:
--------------	-------------

Ing. Jan Božovský	Ing. Tomáš Fial
-------------------	-----------------

Číslo zakázky:	Číslo kopie:
----------------	--------------

75-2020	
---------	--

Datum:	
--------	--

11/2020	
---------	--

Stupeň:	
---------	--

ZPD	
-----	--

Měřítko:	Číslo přílohy:
----------	----------------

1:500	
-------	--

Počet A4:	
-----------	--

2	A.3.b
---	-------

Akce:
**Úprava dopravního režimu na obytnou zónu v ulicích
Na Košíku, Nad Košíkem, U Košíku - Praha 15**

Část/objekt:

B. Výkresová část

Název přílohy:

Situace stavby - U Košíku - obalové křivky